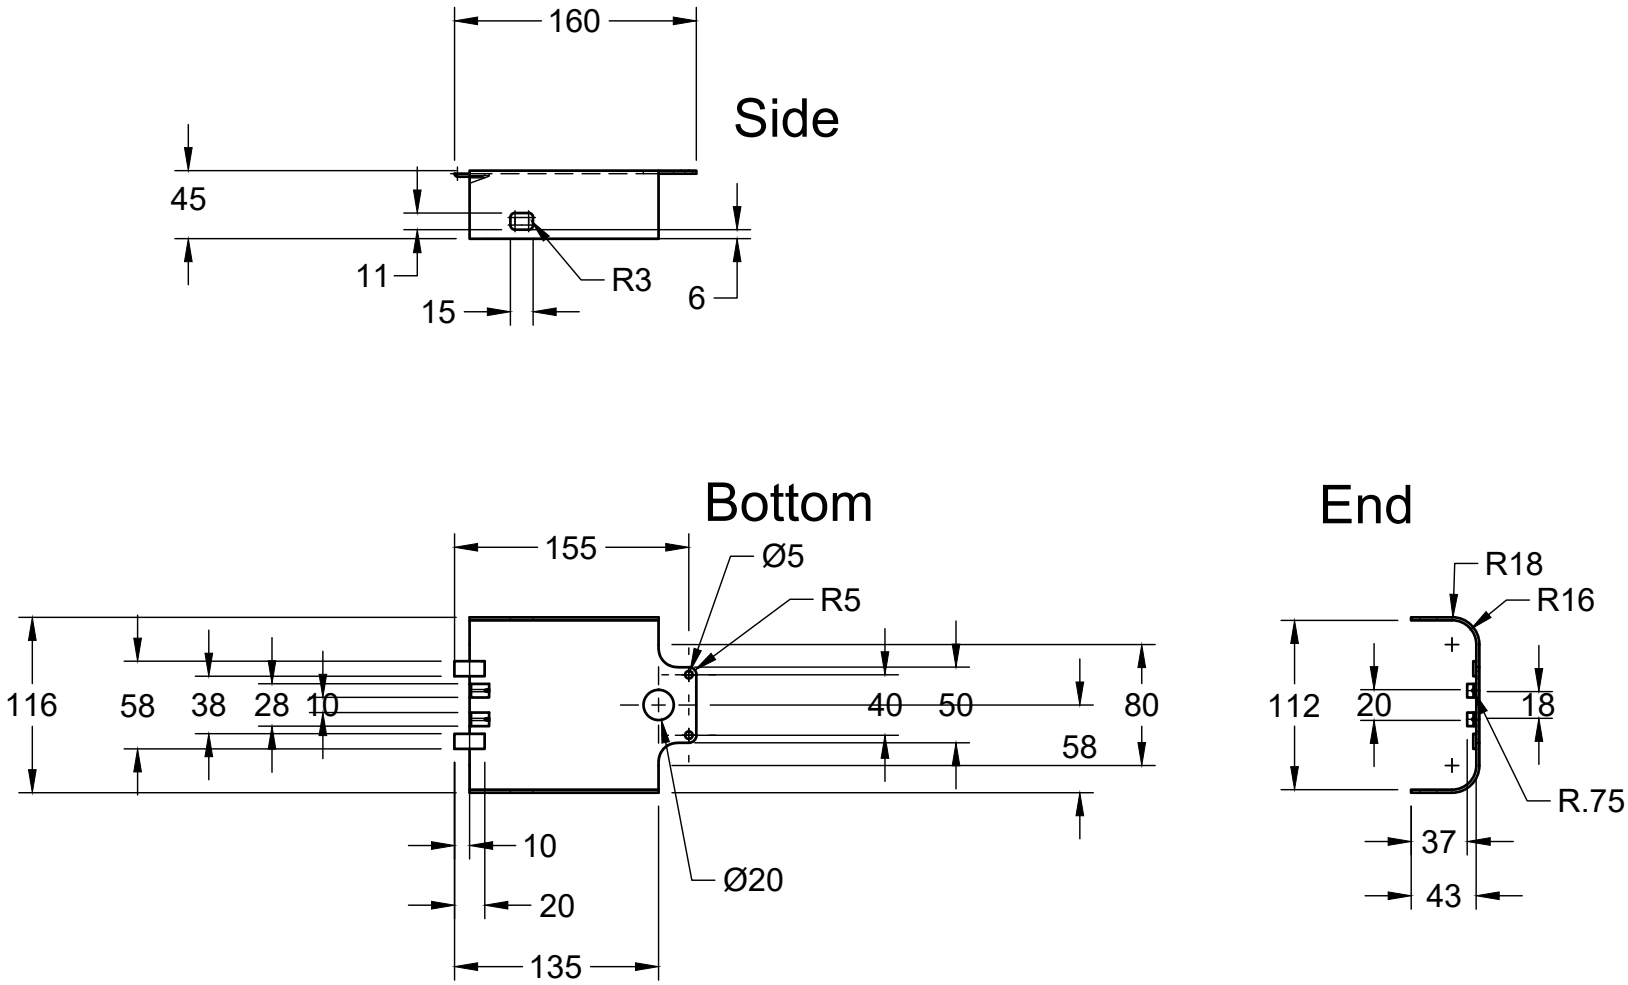

PROJECT Nova				
TITLE Cover_Top_Rear Note: 2mm Wall Thickness				
APPROVED	SIZE	CODE	DWG NO	REV
CHECKED	A			
DRAWN William Nolan 9/10/2025	SCALE 1:5	WEIGHT		SHEET 1/1